
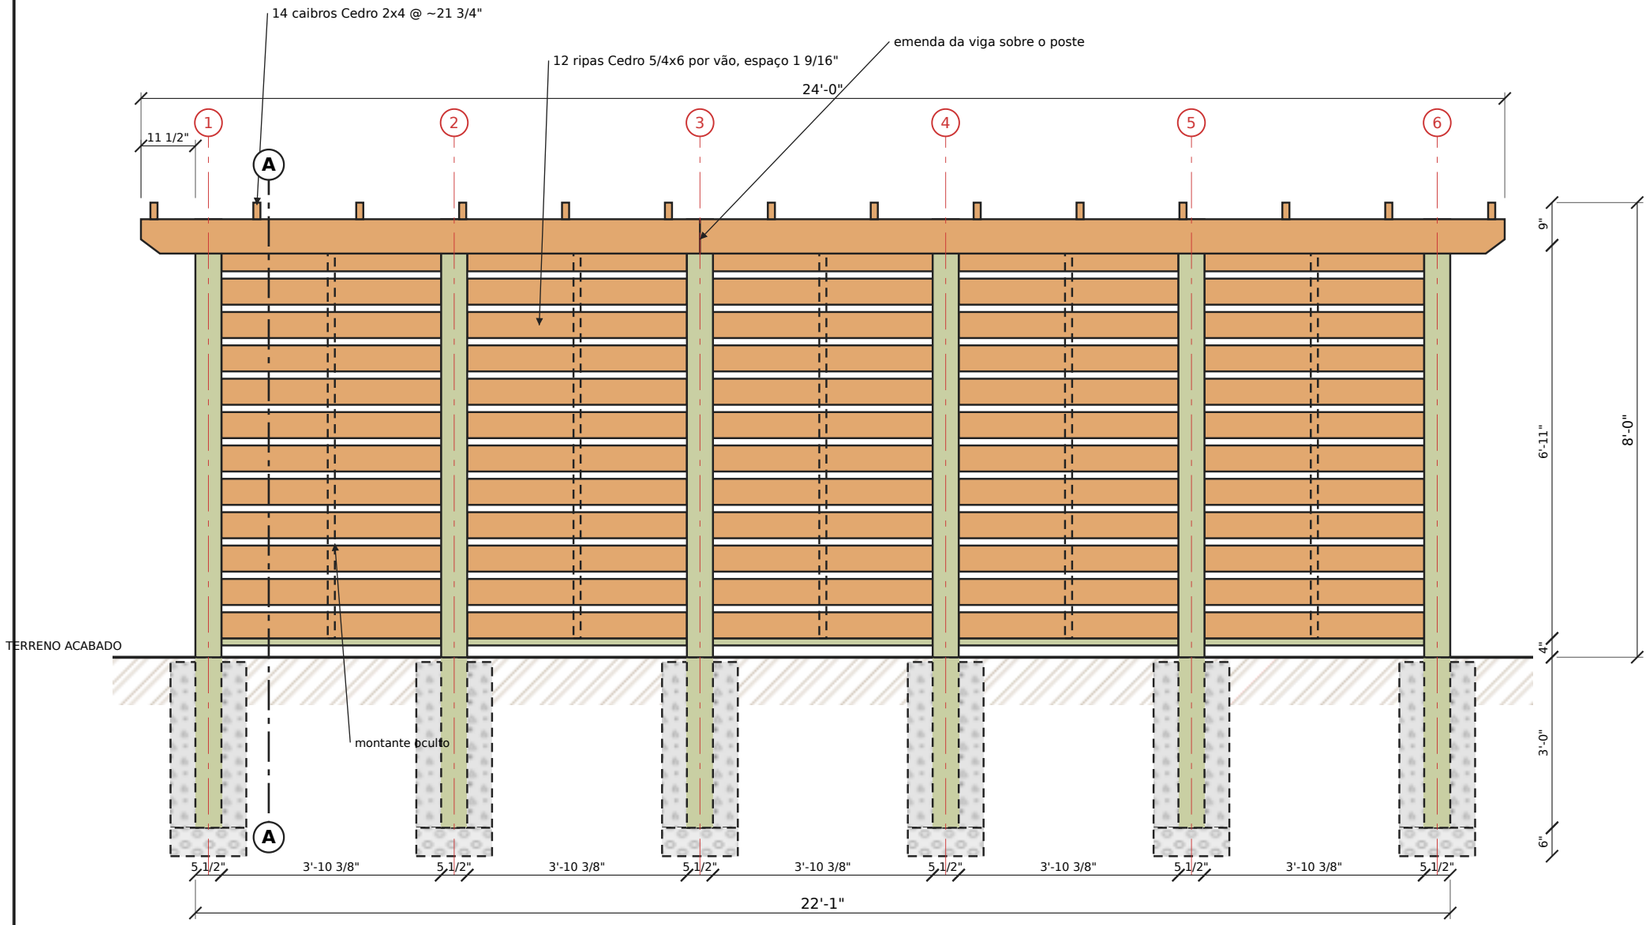


ELEVAÇÃO — LADO DA CASA

ESCALA 1:32 (3/8" = 1'-0")

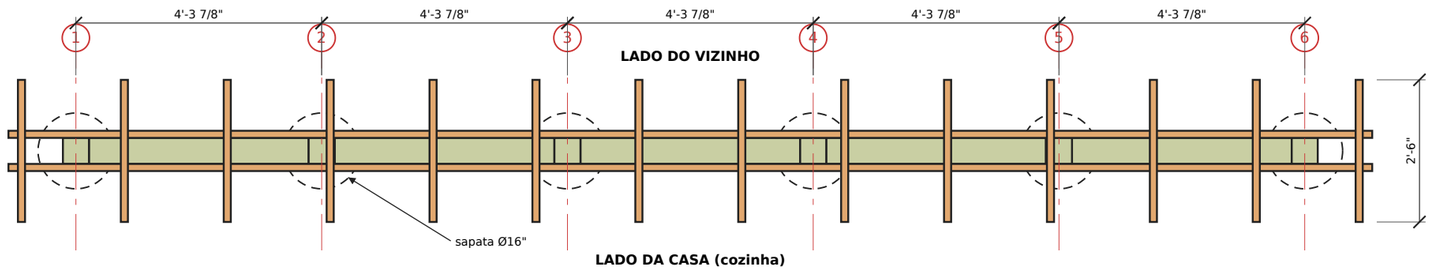

PLANTA — VISTA SUPERIOR

ESCALA 1:32 (3/8" = 1'-0")

NOTAS

1. Comprimento total 22'-1"; 6 postes; vão livre 3'-10 3/8".
2. Postes embutidos 3'-0" em concreto sobre 6" de brita.
3. Ligar para NC811 antes de escavar. Conferir divisa, recuo e HOA.
4. Fixadores: inox no cedro; galvanizado a fogo/inox no PT.
5. Ripas: 12 por vão, espaço 1 9/16"; usar espaçador.

Kitchen Privacy Screen — 265 in x ~8 ft, ripado de cedro + topo pergolado (Cornelius, NC)


Elevação e planta

Data: 2026-11-10 Rev.: 0 Por:

Medidas em polegadas/pés. Madeira: medidas reais (6x6 = 5 1/2").


Conferir no campo antes de cortar. Não é projeto estrutural.

A-1

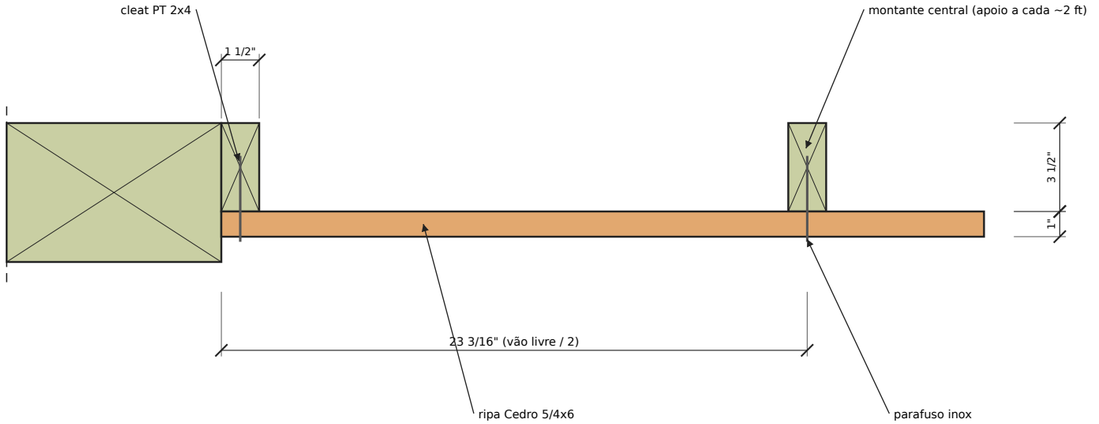


DETALHE 2 — CORTE HORIZONTAL B-B (pela ripa)

ESCALA 1:6

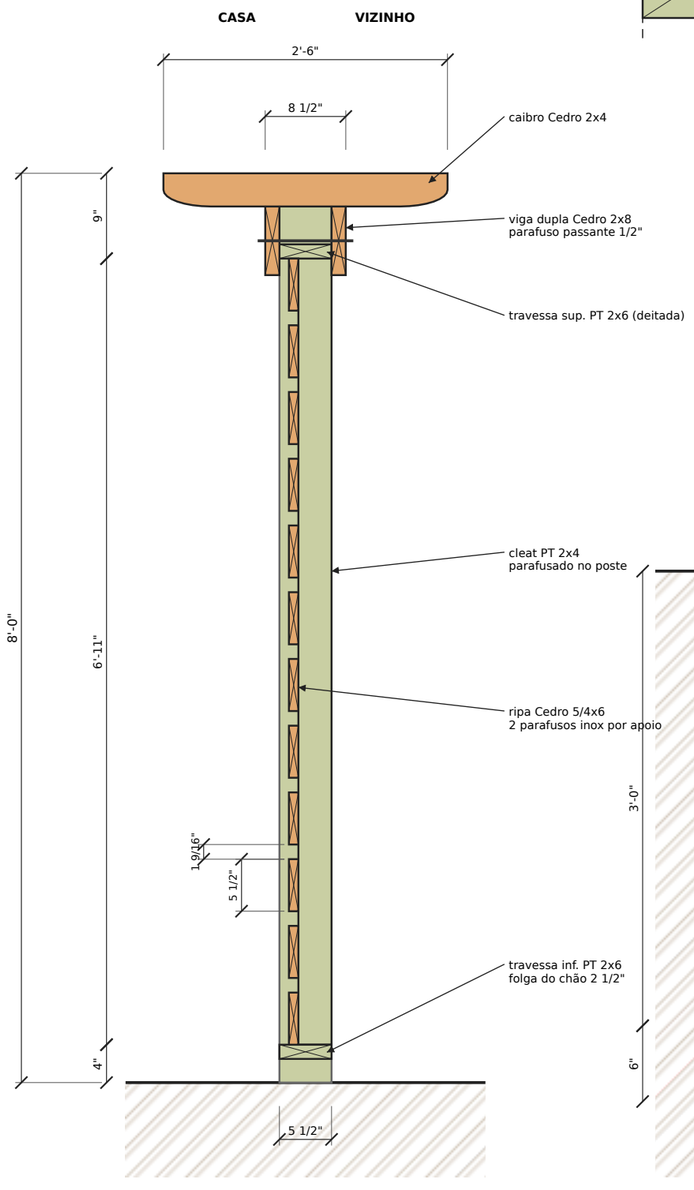


CORTE A-A (no vão, olhando para o poste 1)

ESCALA 1:16 (3/4" = 1'-0")

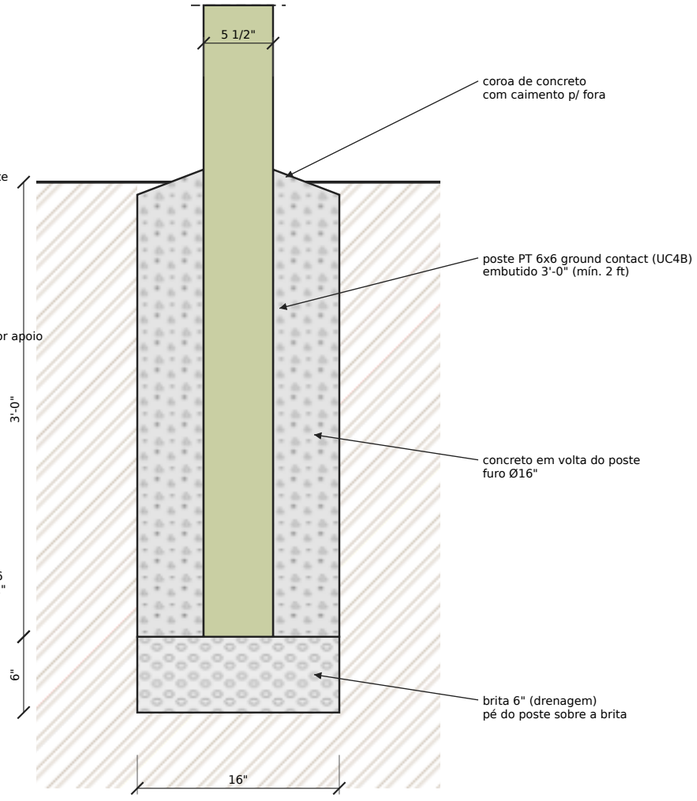

DETALHE 1 — FUNDAÇÃO DO POSTE

ESCALA 1:12 (1" = 1'-0")

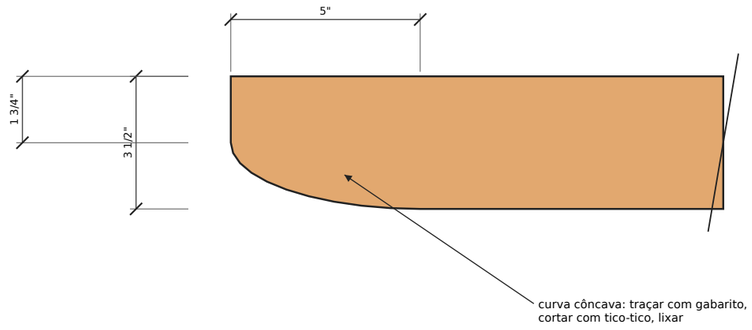

DETALHE 3 — PONTA DO CAIBRO / VIGA

ESCALA 1:4 (3" = 1'-0")

LISTA DE PEÇAS

Marca	Peça	Material	Qtd	Compr.	Obs.
P	Poste	PT 6x6 ground contact (UC4B)	6	10'-8 1/2"	embutir 3'-0"
TI	Travessa inferior	PT 2x6	5	3'-10 3/8"	deitada
TS	Travessa superior	PT 2x6	5	3'-10 3/8"	deitada, atrás das vigas
C	Cleat	PT 2x4	10	6'-11"	nas faces dos postes
M	Montante central	PT 2x4	5	6'-11"	meio do vão
R	Ripa	Cedro 5/4x6	60	3'-10 3/8"	12/vão, espaço 1 9/16"
V	Viga (2 linhas x 2 peças)	Cedro 2x8	4	12'-0"	emenda sobre poste
K	Caibro decorativo	Cedro 2x4	14	2'-6"	pontas recortadas

Kitchen Privacy Screen — 265 in x ~8 ft, ripado de cedro + topo pergolado (Cornelius, NC)

Cortes e detalhes

Data: 2026-11-10 Rev.: 0 Por:

Medidas em polegadas/pés. Madeira: medidas reais (6x6 = 5 1/2").

Conferir no campo antes de cortar. Não é projeto estrutural.

A-2