
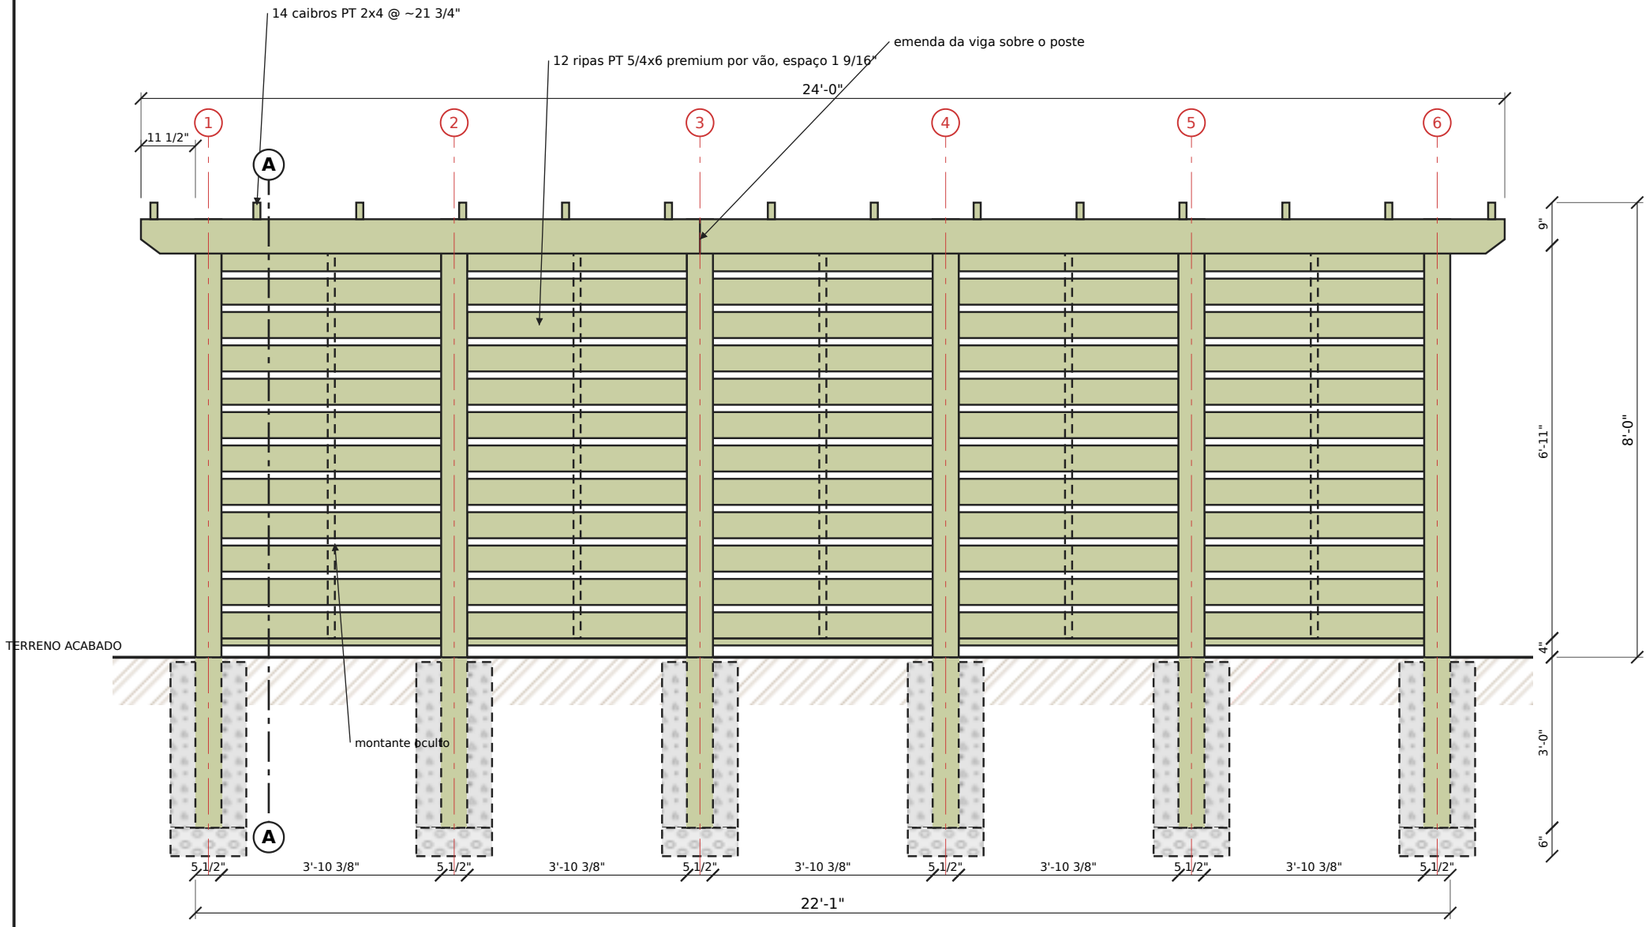



## ELEVAÇÃO — LADO DA CASA

ESCALA 1:32 (3/8" = 1'-0")

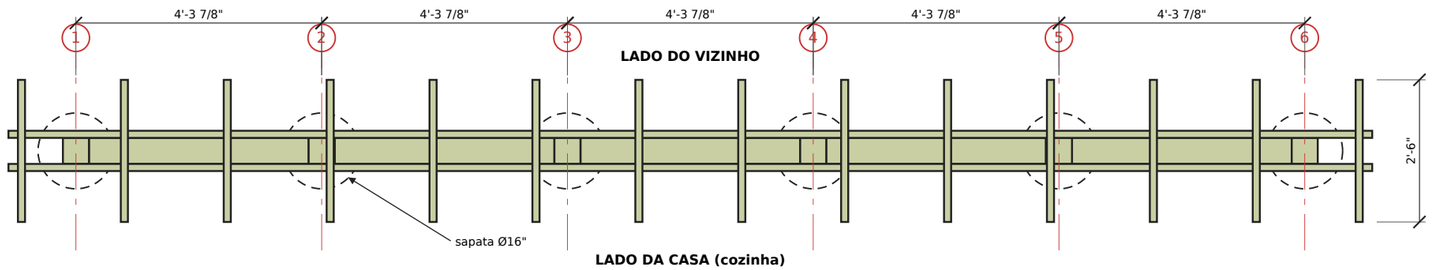


## PLANTA — VISTA SUPERIOR

ESCALA 1:32 (3/8" = 1'-0")

**NOTAS**

1. Comprimento total 22'-1"; 6 postes; vão livre 3'-10 3/8".
2. Postes embutidos 3'-0" em concreto sobre 6" de brita.
3. Ligar para NC811 antes de escavar. Conferir divisa, recuo e HOA.
4. Fixadores: inox no cedro; galvanizado a fogo/inox no PT.
5. Ripas: 12 por vão, espaço 1 9/16"; usar espaçador.

**Kitchen Privacy Screen — 265 in x ~8 ft, 100% pinus autoclavado (PT) + topo pergolado (Cornelius, NC)**


**Elevação e planta**

Data: 2026-11-10 Rev.: 0 Por:

Medidas em polegadas/pés. Madeira: medidas reais (6x6 = 5 1/2").


Conferir no campo antes de cortar. Não é projeto estrutural.

**A-1**

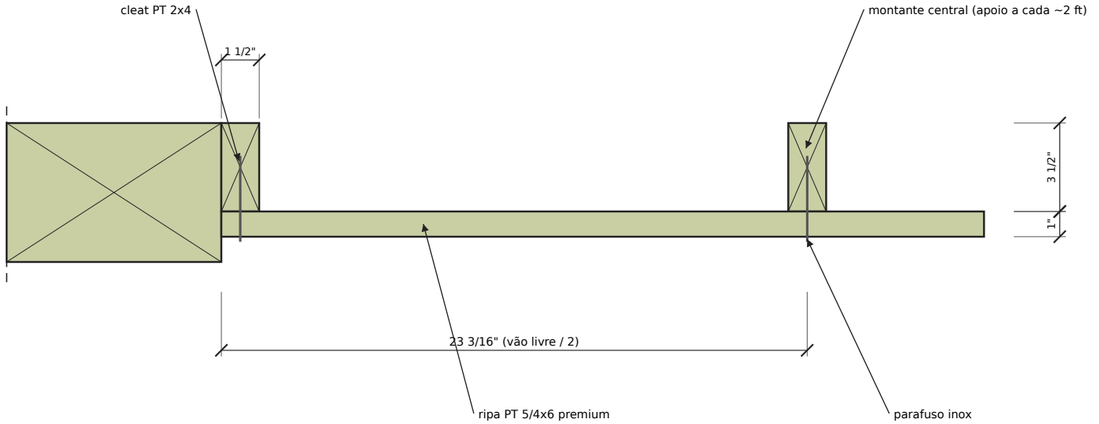



## DETALHE 2 — CORTE HORIZONTAL B-B (pela ripa)

ESCALA 1:6

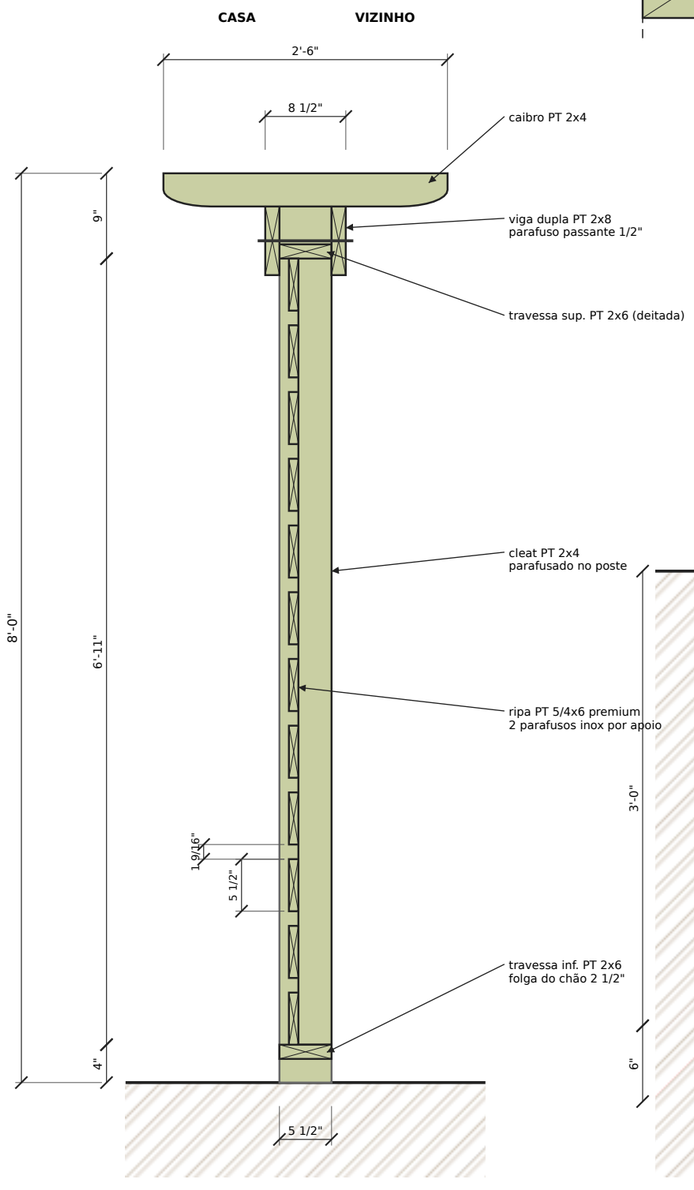



## CORTE A-A (no vão, olhando para o poste 1)

ESCALA 1:16 (3/4" = 1'-0")

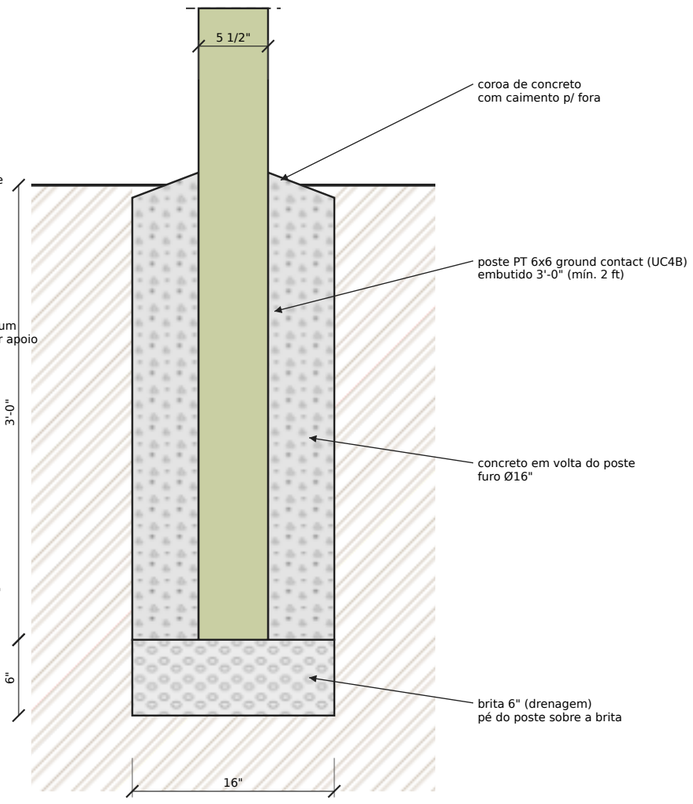


## DETALHE 1 — FUNDAÇÃO DO POSTE

ESCALA 1:12 (1" = 1'-0")

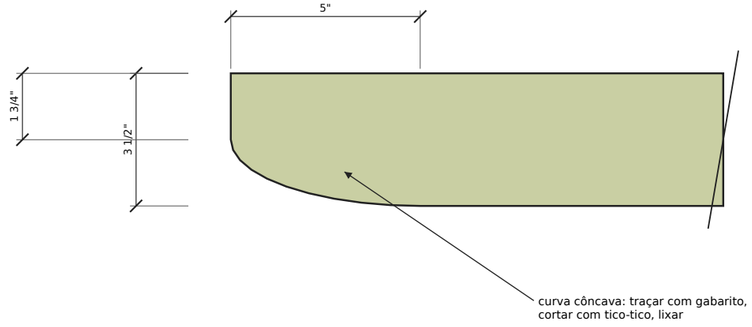


## DETALHE 3 — PONTA DO CAIBRO / VIGA

ESCALA 1:4 (3" = 1'-0")

### LISTA DE PEÇAS

| Marca | Peça | Material | Qtd | Compr. | Obs. |
|---|---|---|---|---|---|
| P | Poste | PT 6x6 ground contact (UC4B) | 6 | 10'-8 1/2" | embutir 3'-0" |
| TI | Travessa inferior | PT 2x6 | 5 | 3'-10 3/8" | deitada |
| TS | Travessa superior | PT 2x6 | 5 | 3'-10 3/8" | deitada, atrás das vigas |
| C | Cleat | PT 2x4 | 10 | 6'-11" | nas faces dos postes |
| M | Montante central | PT 2x4 | 5 | 6'-11" | meio do vão |
| R | Ripa | PT 5/4x6 premium | 60 | 3'-10 3/8" | 12/vão, espaço 1 9/16" |
| V | Viga (2 linhas x 2 peças) | PT 2x8 | 4 | 12'-0" | emenda sobre poste |
| K | Caibro decorativo | PT 2x4 | 14 | 2'-6" | pontas recortadas |

**Kitchen Privacy Screen — 265 in x ~8 ft, 100% pinus autoclavado (PT) + topo pergolado (Cornelius, NC)**

## Cortes e detalhes

Data: 2026-11-10 Rev.: 0 Por:

Medidas em polegadas/pés. Madeira: medidas reais (6x6 = 5 1/2").

Conferir no campo antes de cortar. Não é projeto estrutural.

**A-2**