
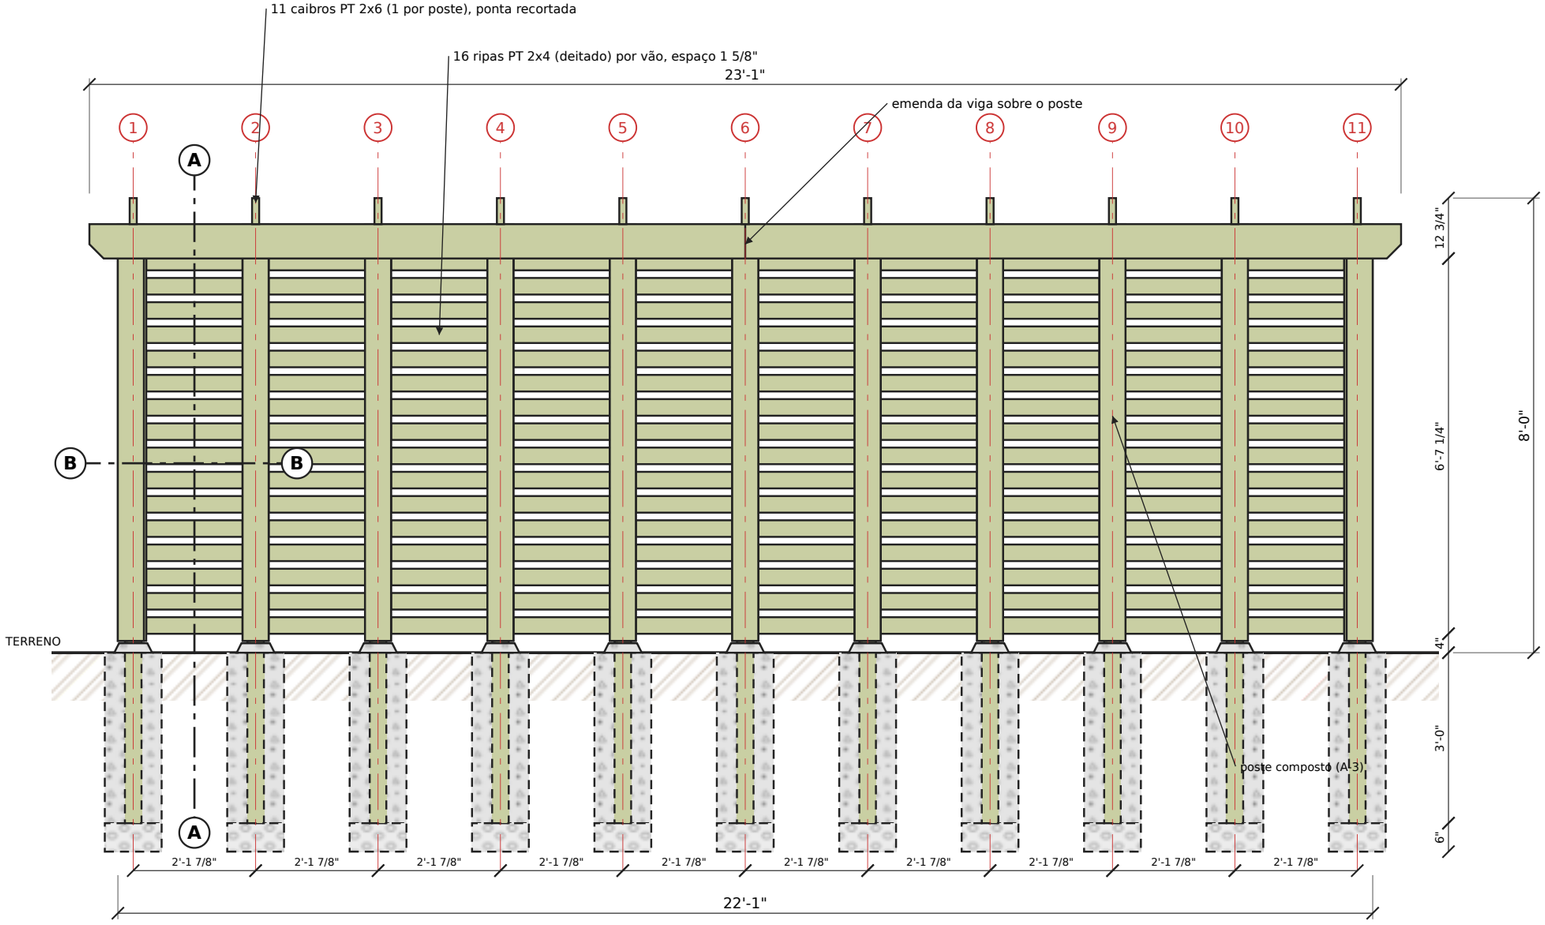



ELEVAÇÃO — LADO DO VIZINHO

ESCALA 1:32 (3/8" = 1'-0")

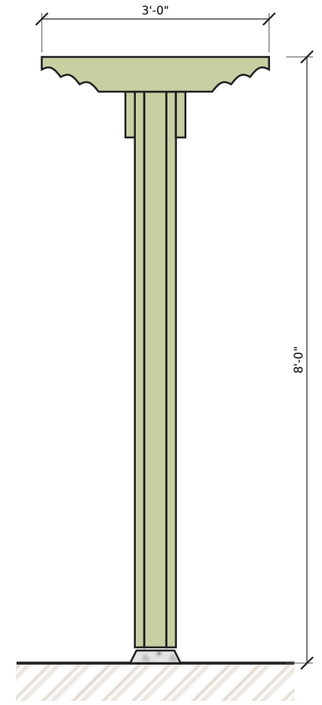

ELEVAÇÃO LATERAL (extremidade)

ESCALA 1:24 (1/2" = 1'-0")

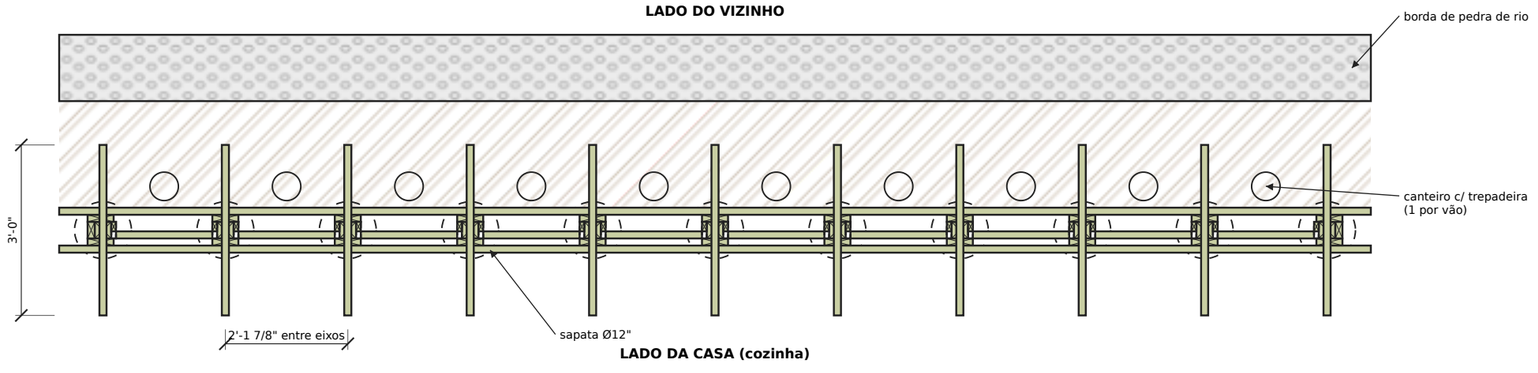

PLANTA — VISTA SUPERIOR

ESCALA 1:32 (3/8" = 1'-0")

NOTAS

1. Comprimento 22'-1"; 11 postes a 2'-1 7/8" entre eixos; vão livre 20 3/8".
2. Núcleo dos postes embutido 3'-0" em concreto sobre 6" de brita.
3. Ligar para NC811 antes de escavar. Conferir divisa, recuo e HOA.
4. Fixadores: inox no cedro; galvanizado a fogo/inox no PT.
5. Ripas: 16 por vão, espaço 1 5/8" dado pelo serrilhado.
6. Postes intermediários 5 1/2" (alinhados com a face 2x6); postes de ponta 6".

Kitchen Privacy Screen — 265 in x ~8 ft, 100% pinus autoclavado (PT) + topo pergolado (Cornelius, NC)


Elevação e planta

Data: 2026-11-10 Rev.: 4 Por:

Medidas em polegadas/pés. Madeira: medidas reais (6x6 = 5 1/2").


Conferir no campo antes de cortar. Não é projeto estrutural.

A-1

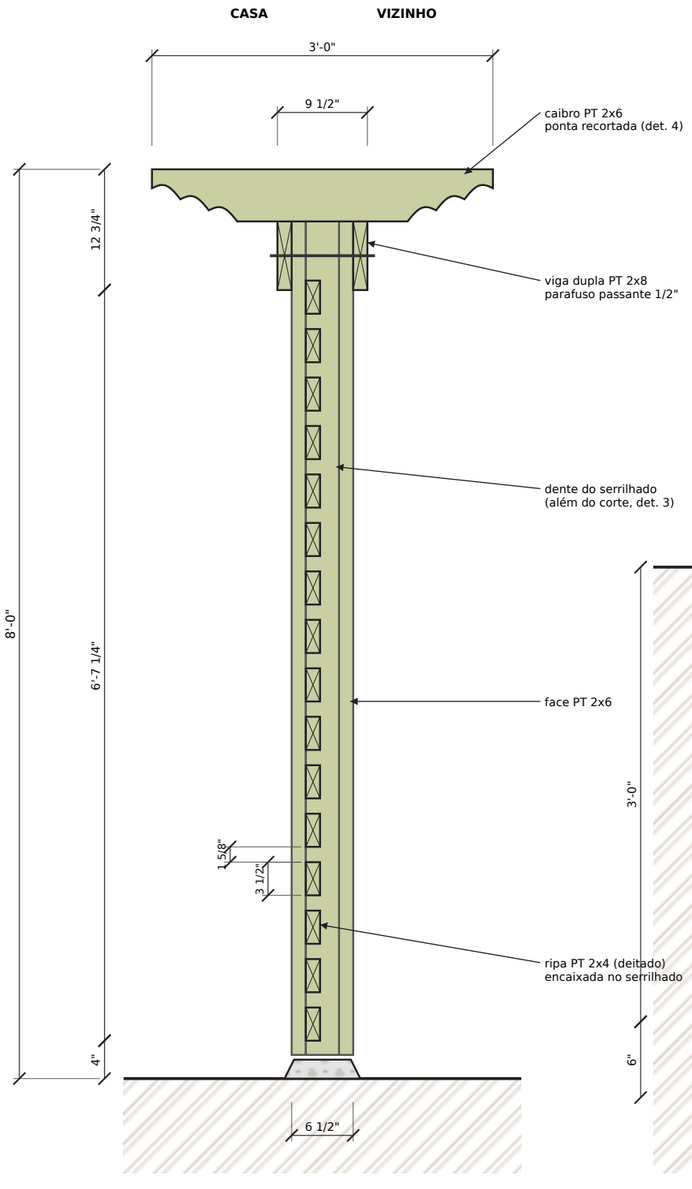


CORTE A-A (meio do vão, olhando o poste 1)

ESCALA 1:16 (3/4" = 1'-0")

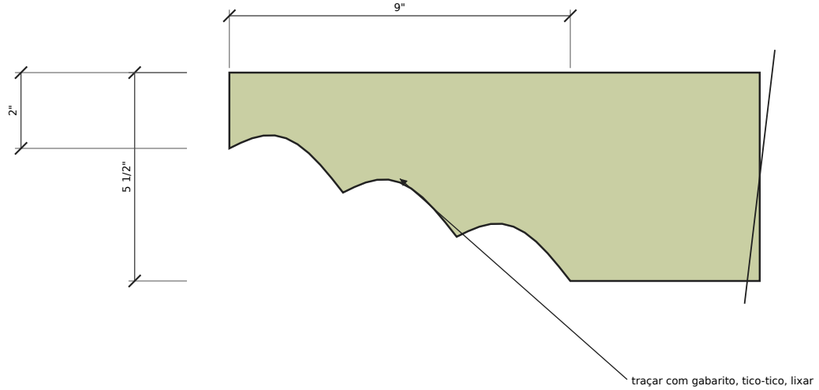


DETALHE 4 — PONTA DO CAIBRO

ESCALA 1:4 (3" = 1'-0")

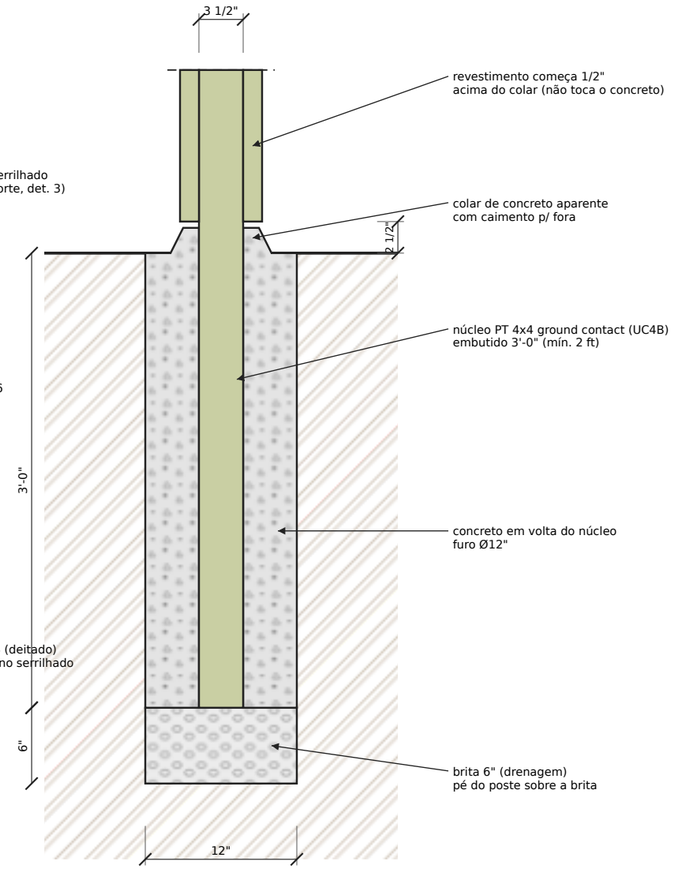

DETALHE 1 — FUNDAÇÃO DO POSTE

ESCALA 1:12 (1" = 1'-0")

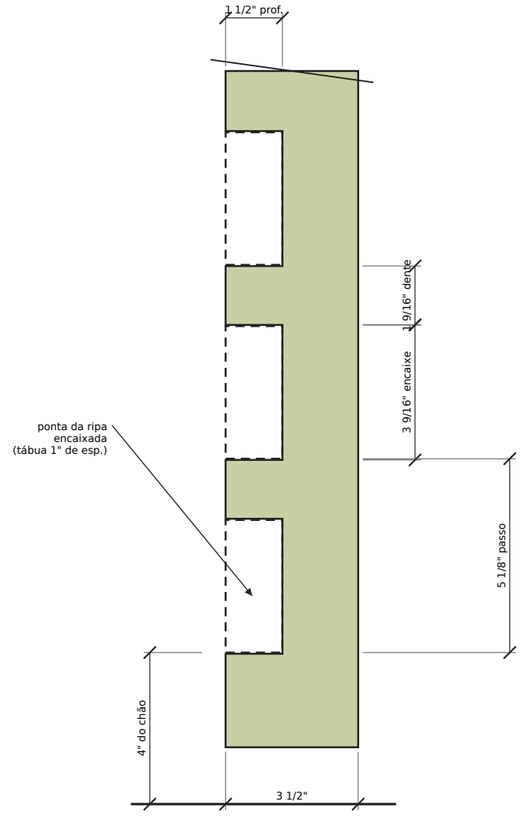

DETALHE 3 — SERRILHADO (vista do vão)

ESCALA 1:4 (3" = 1'-0")

LISTA DE PEÇAS

Marca	Peça	Material	Qtd	Compr.	Obs.
N	Núcleo do poste	PT 4x4 ground contact (UC4B)	11	10'-6 1/2"	embutir 3'-0"
F	Face do poste	PT 2x6	22	7'-4"	casa + vizinho
S	Lateral serrilhada	PT 5/4 (1") serrilhado	20	7'-4"	16 encaixes; ripar p/ 3 1/2"
L	Lateral lisa	PT 2x6 lisa	2	7'-4"	postes 1 e 11, lado externo
R	Ripa	PT 2x4 (deitado)	160	22 1/8"	16/vão, espaço 1 5/8"
V	Viga (2 linhas x 2)	PT 2x8	4	11'-6 1/2" + 11'-6 1/2"	emenda sobre poste
K	Caibro decorativo	PT 2x6	11	3'-0"	pontas recortadas

Kitchen Privacy Screen — 265 in x ~8 ft, 100% pinus autoclavado (PT) + topo pergolado (Cornelius, NC)


Cortes e detalhes

Data: 2026-11-10 Rev.: 4 Por:

Medidas em polegadas/pés. Madeira: medidas reais (6x6 = 5 1/2").


Conferir no campo antes de cortar. Não é projeto estrutural.

A-2

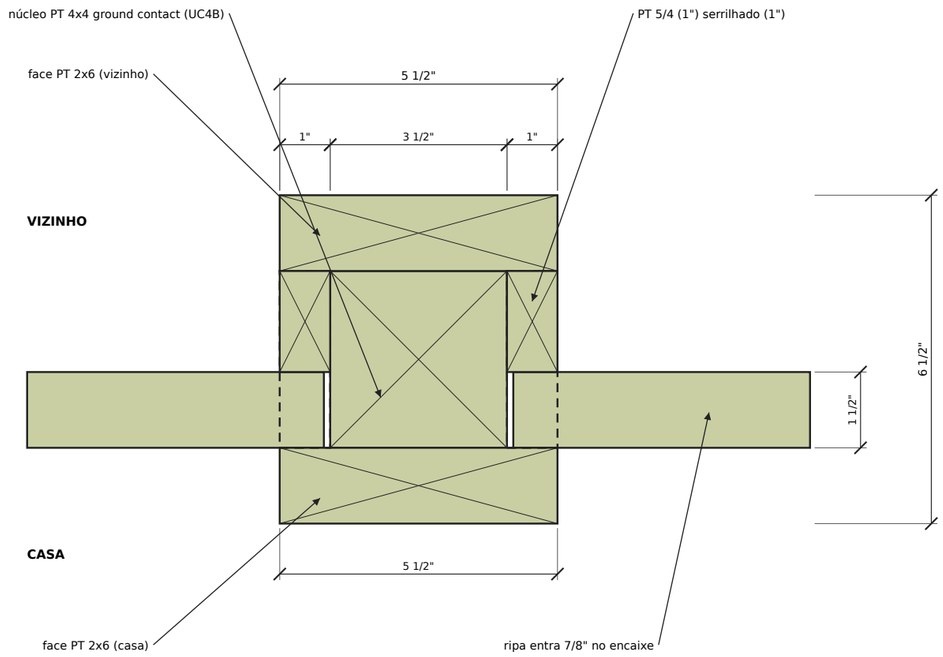

DETALHE 2a — POSTE INTERMEDIÁRIO, CORTE B-B

ESCALA 1:3

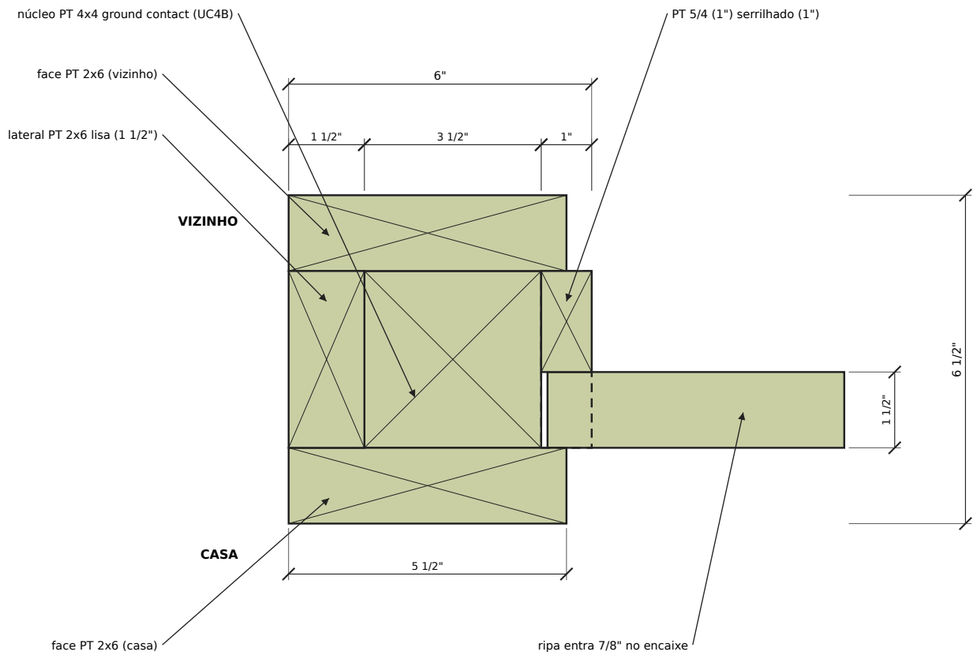

DETALHE 2b — POSTE DE PONTA (1 e 11)

ESCALA 1:3

#	SEQUÊNCIA DE MONTAGEM
1	Locar os 11 eixos a 2'-1 7/8"; furos Ø12" x 3'-6"; 6" de brita no fundo.
2	Prumar e alinhar os núcleos 4x4 com escoras e linha; concretar; colar com caimento. Curar 48 h.
3	Cortar todos os núcleos na mesma altura (7'-6 1/2" acima do terreno), com nível laser ou mangueira.
4	Fabricar os 20 serrilhados (1" x 3 1/2") juntos, com gabarito: 16 encaixes de 3 9/16" x 1 1/2", passo 5 1/8".
5	Fixar as faces 2x6 do LADO DO VIZINHO nos núcleos (parafuso inox, cola PU).
6	Fixar os serrilhados nas laterais dos núcleos (encaixes para o lado da casa) e as laterais lisas 2x6 nos postes de ponta.
7	Encaixar as ripas pelo lado da casa, de baixo para cima; 1 parafuso inox por ponta no serrilhado.
8	Fechar com as faces 2x6 do LADO DA CASA: elas travam as ripas nos encaixes.
9	Vigas duplas 2x8 com parafuso passante 1/2" por poste (emenda sobre o poste do meio).
10	Caibros com ponta recortada sobre as vigas, 1 por poste; parafuso estrutural.

Kitchen Privacy Screen — 265 in x ~8 ft, 100% pinus autoclavado (PT) + topo pergolado (Cornelius, NC)

Poste composto com serrilhado

Data: 2026-11-10 Rev.: 4 Por:

Medidas em polegadas/pés. Madeira: medidas reais (6x6 = 5 1/2").

Conferir no campo antes de cortar. Não é projeto estrutural.

A-3